
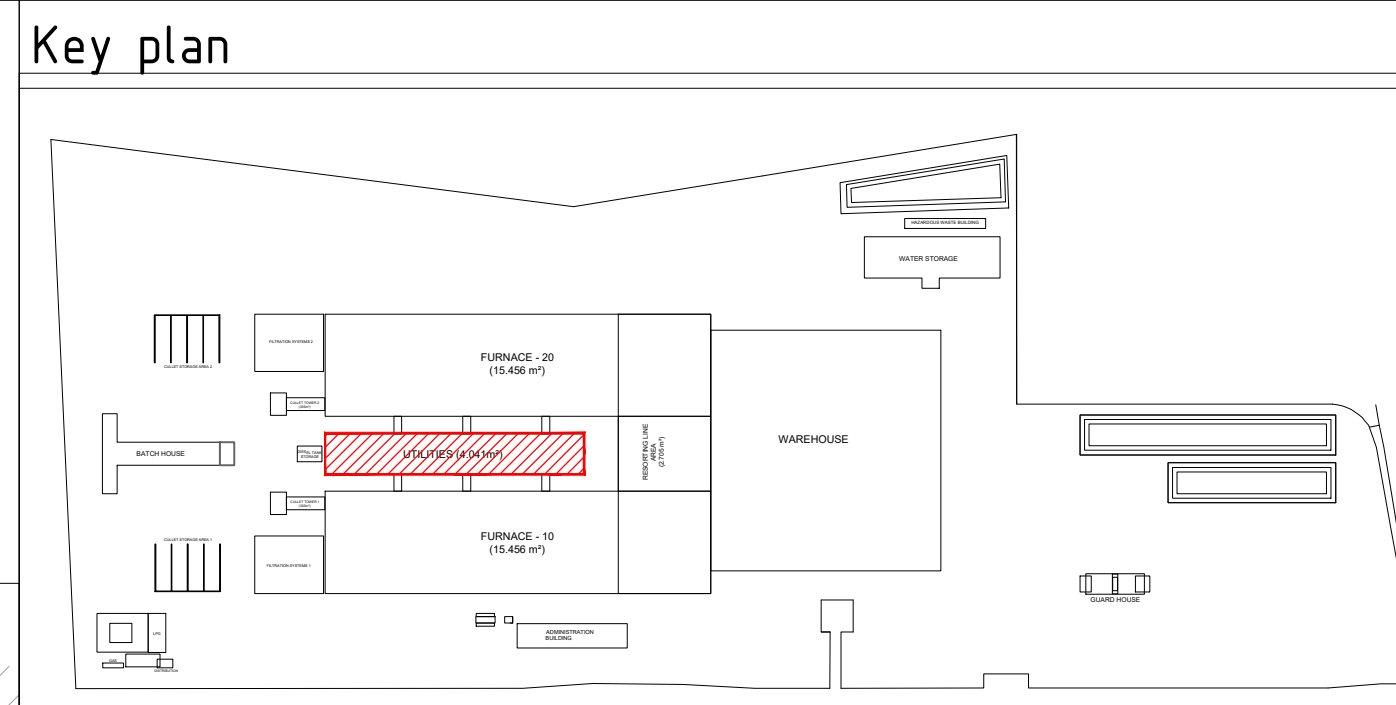


 

- Notes
- References
- 1. Tender Submission: BE-LOM-DIM-UTB-ELC-MV-BM
 - 2. Architectural Submission: BA_V001_P_N_8_Spikes (R0724)
 - 3. MV Distribution System Riser: DNEB-PNEP20-AB-XXX-SPT-5255

A.02	23/06/2025	AT	SB	For External Review
A.01	13/06/2025	BA	HU	For External Review
REV	DATE	BY	CHK	DESCRIPTION
dt construction CNER Marie Poppelinstraat 3920 Lommel, Belgium Description UTILITY BUILDING MV DISTRIBUTION SYSTEM GROUND FLOOR (0.00 LEVEL) Project CNBE Director PNEP20 Building UB Level 000 Category LAY Doc. Number 5246 This drawing is the property of CNER. It is not to be used for any other purpose without the written consent of CNER. Source Doc. No. 5246 Format A0+ Scale 1/1000 Revision A.02				