


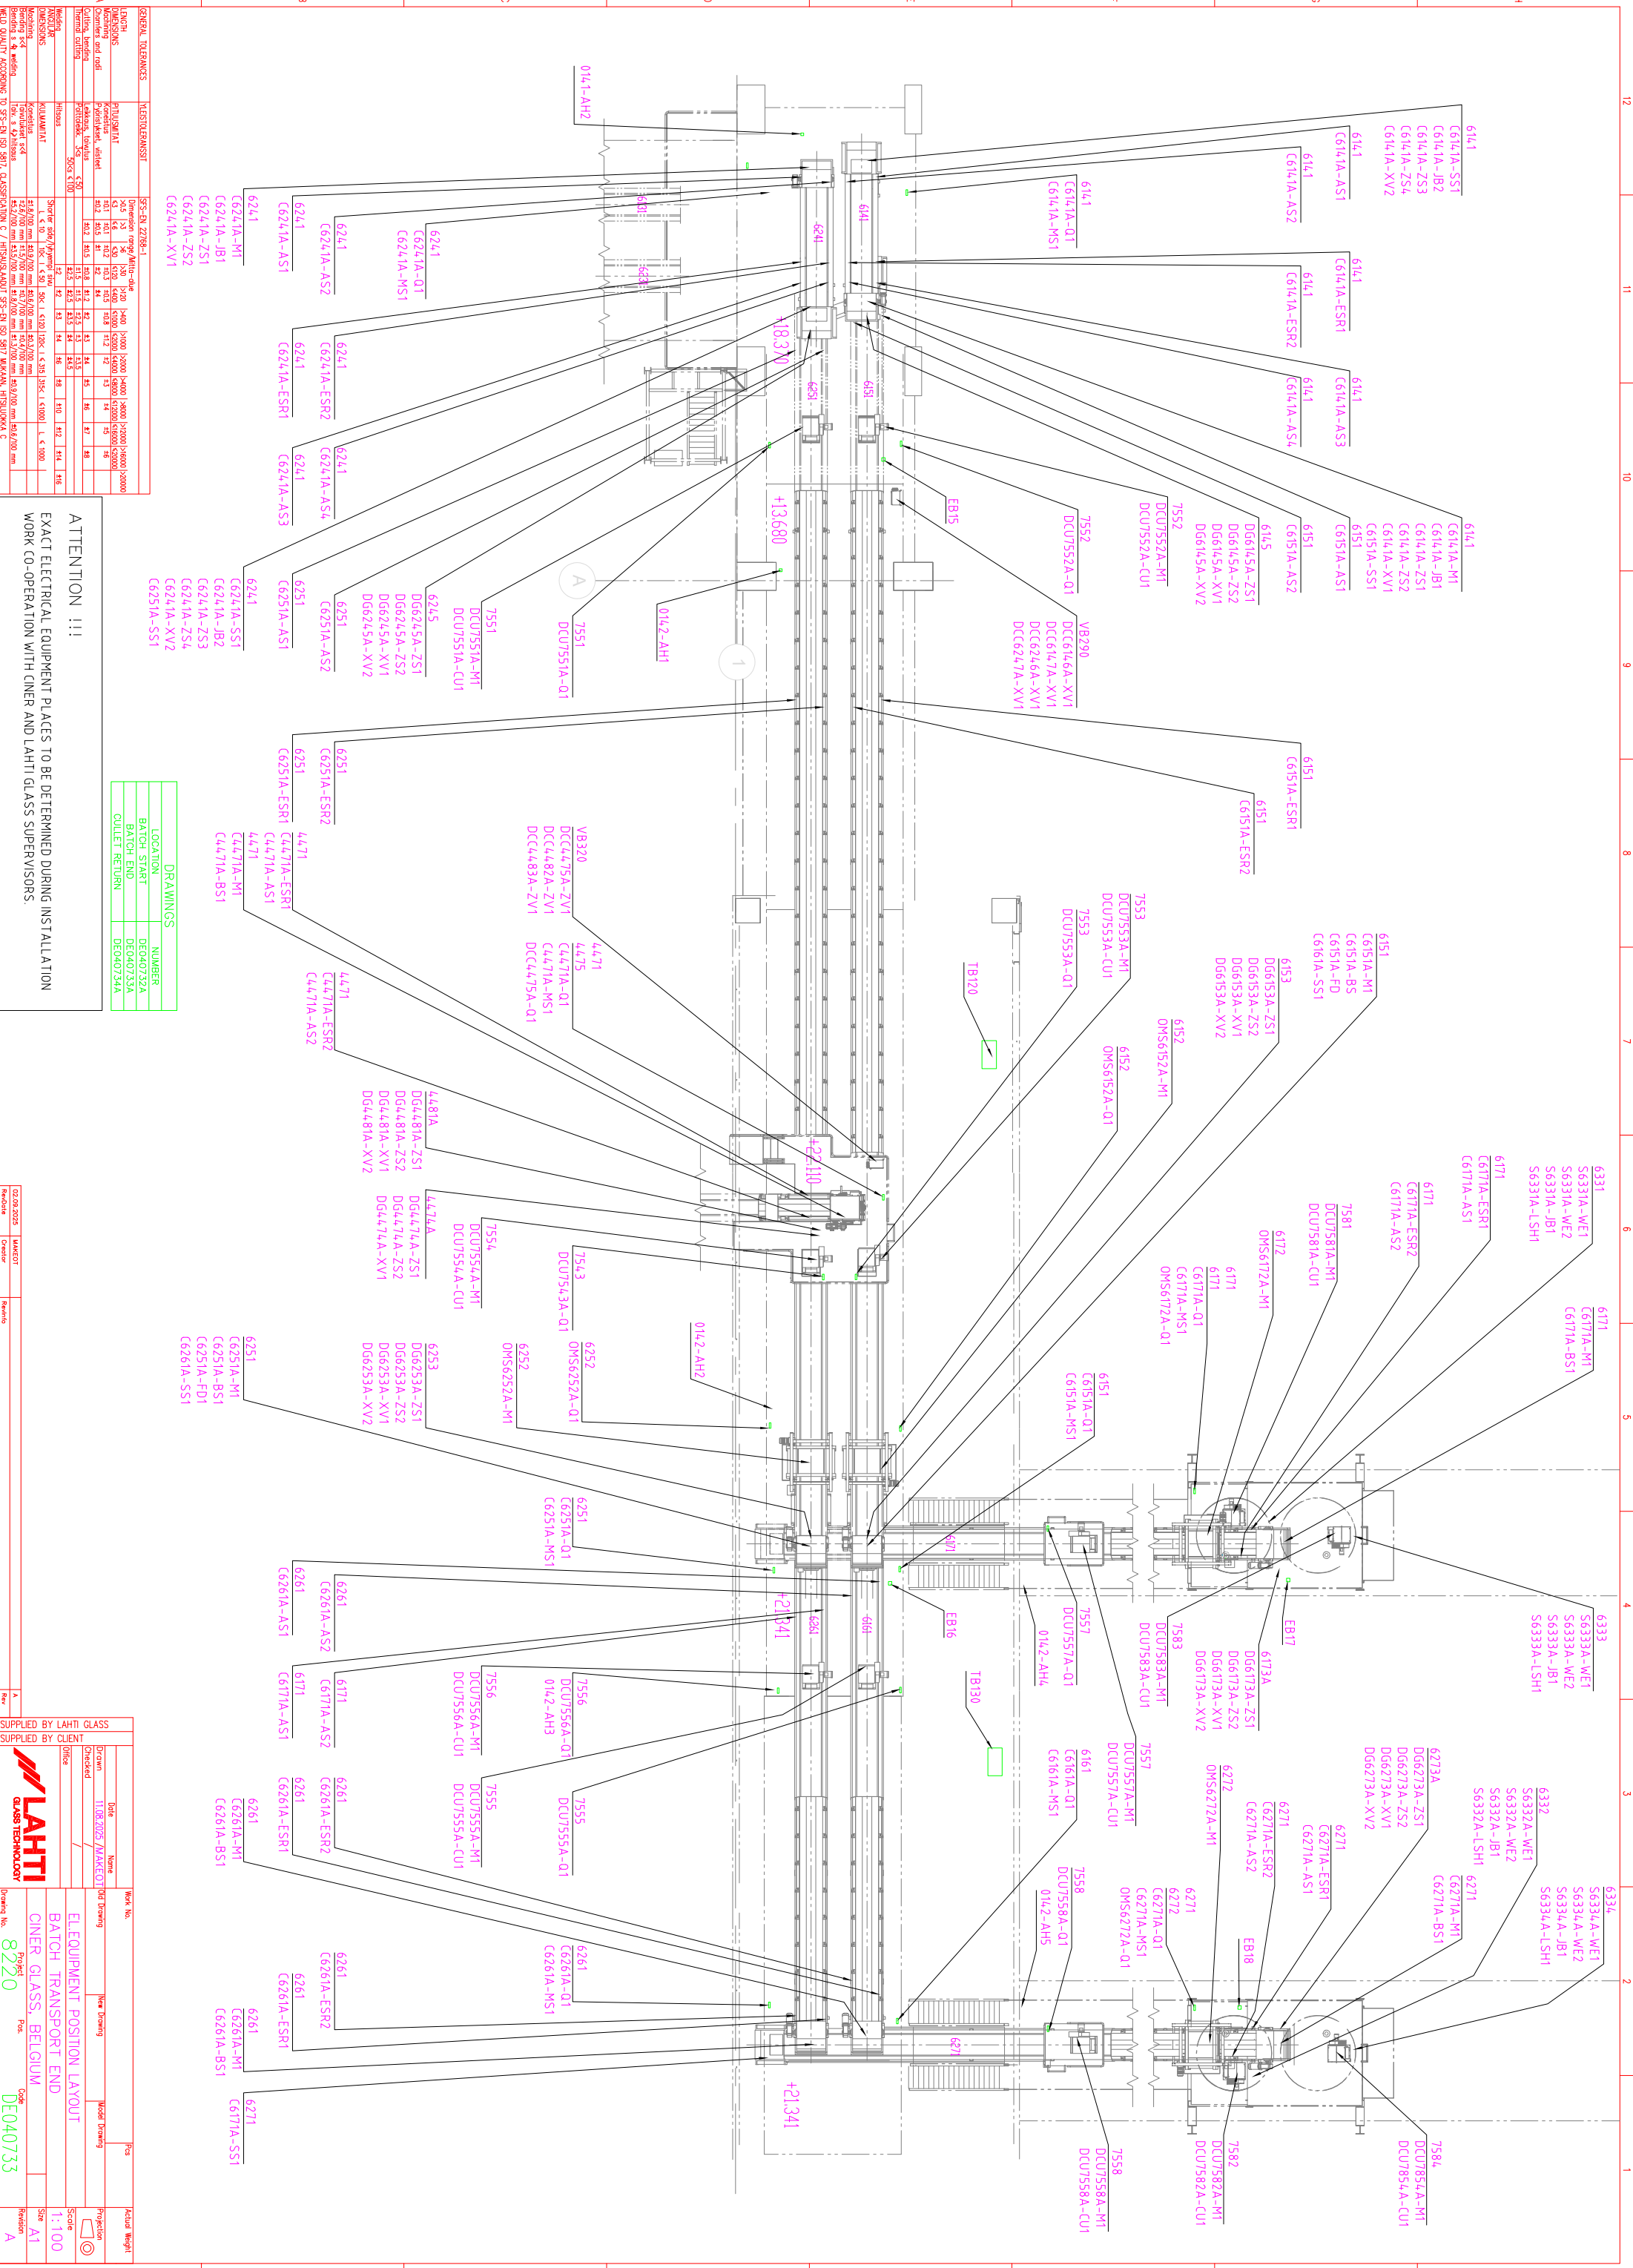

ATTENTION !!!
EXACT ELECTRICAL EQUIPMENT PLACES TO BE DETERMINED DURING INSTALLATION
WORK CO-OPERATION WITH CNER AND LAHTI GLASS SUPERVISORS.

DRAWINGS	
LOCATION	NUMBER
BATCH START	DE040732A
BATCH END	DE040733A
CULLET RETURN	DE040734A

Module	Unit/OT	Remarks

SUPPLIED BY LAHTI GLASS		SUPPLIED BY CLIENT	
Office		Date	
Checked		Name	
11/08/2025		MALEOTI	
Order No.		Work No.	
Project		Batch Drawing	
Pos.		Net Drawing	
Code		Model Drawing	
8220		DE40733	
Revision		Projection	
A			
Scale		1:100	
Size		A1	
Revision		A	