


This drawing and the design shown therein is the property of
Lahti Glass Technology Oy. Any duplication or use of this print for
purposes other than for which it was furnished is hereby prohibited.

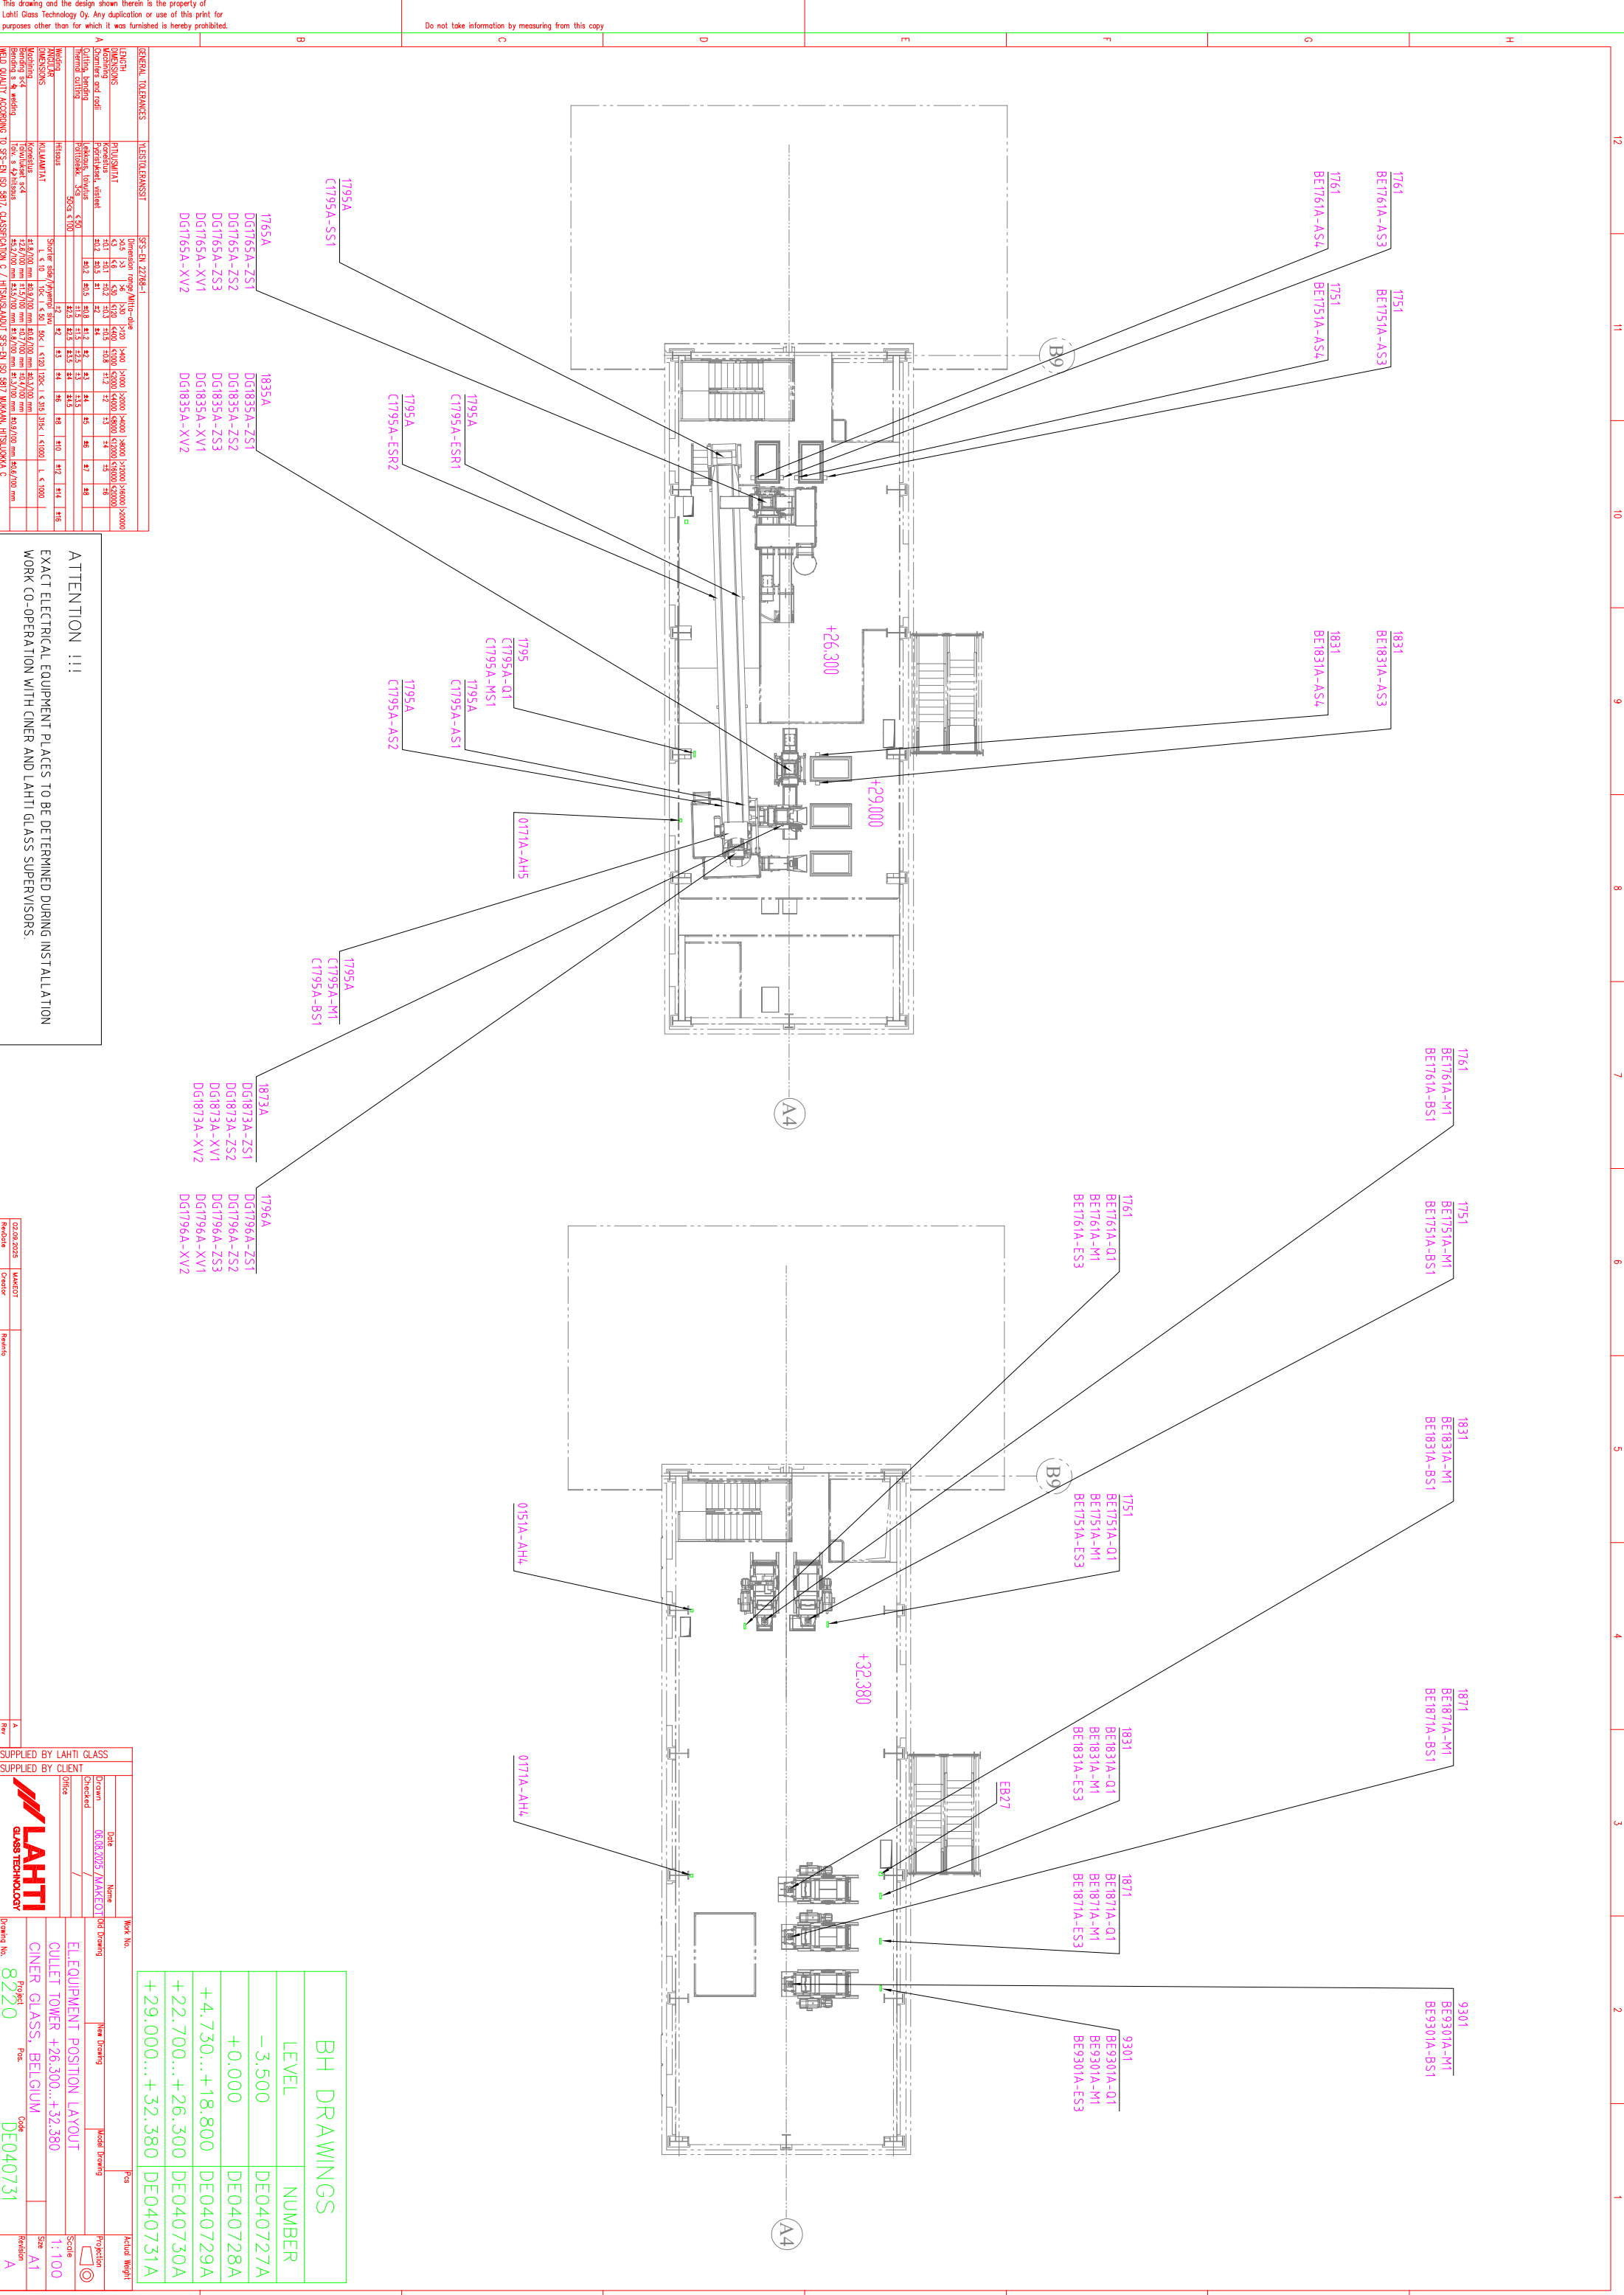

ATTENTION !!!
EXACT ELECTRICAL EQUIPMENT PLACES TO BE DETERMINED DURING INSTALLATION
WORK CO-OPERATION WITH CINER AND LAHTI GLASS SUPERVISORS.

02.09.2025	MAKOT	Rev	0
Project	Client	Rev	0
SUPPLIED BY LAHTI GLASS			
SUPPLIED BY CLIENT			
Drawn	Date	Rev	0
Checked	06.08.2025 / AAK/EO1	Rev	0
Office		Rev	0
EL.EQUIPMENT POSITION LAYOUT			
CULLET TOWER +26.300..+32.380			
CINER GLASS. BELGIUM			
Project	Rev	Scale	1:100
02.09.2025	8220	DE040731	A
Printed	29.09.2025		

BH DRAWINGS	
LEVEL	NUMBER
-3.500	DE040727A
+0.000	DE040728A
+4.730...+18.800	DE040729A
+22.700...+26.300	DE040730A
+29.000...+32.380	DE040731A