This drawing and the design shown therein is the property of Lahti Glass Technology Oy. Any duplication or use of this print for purposes other than for which it was furnished is hereby prohibited.

Do not take information by measuring from this copy

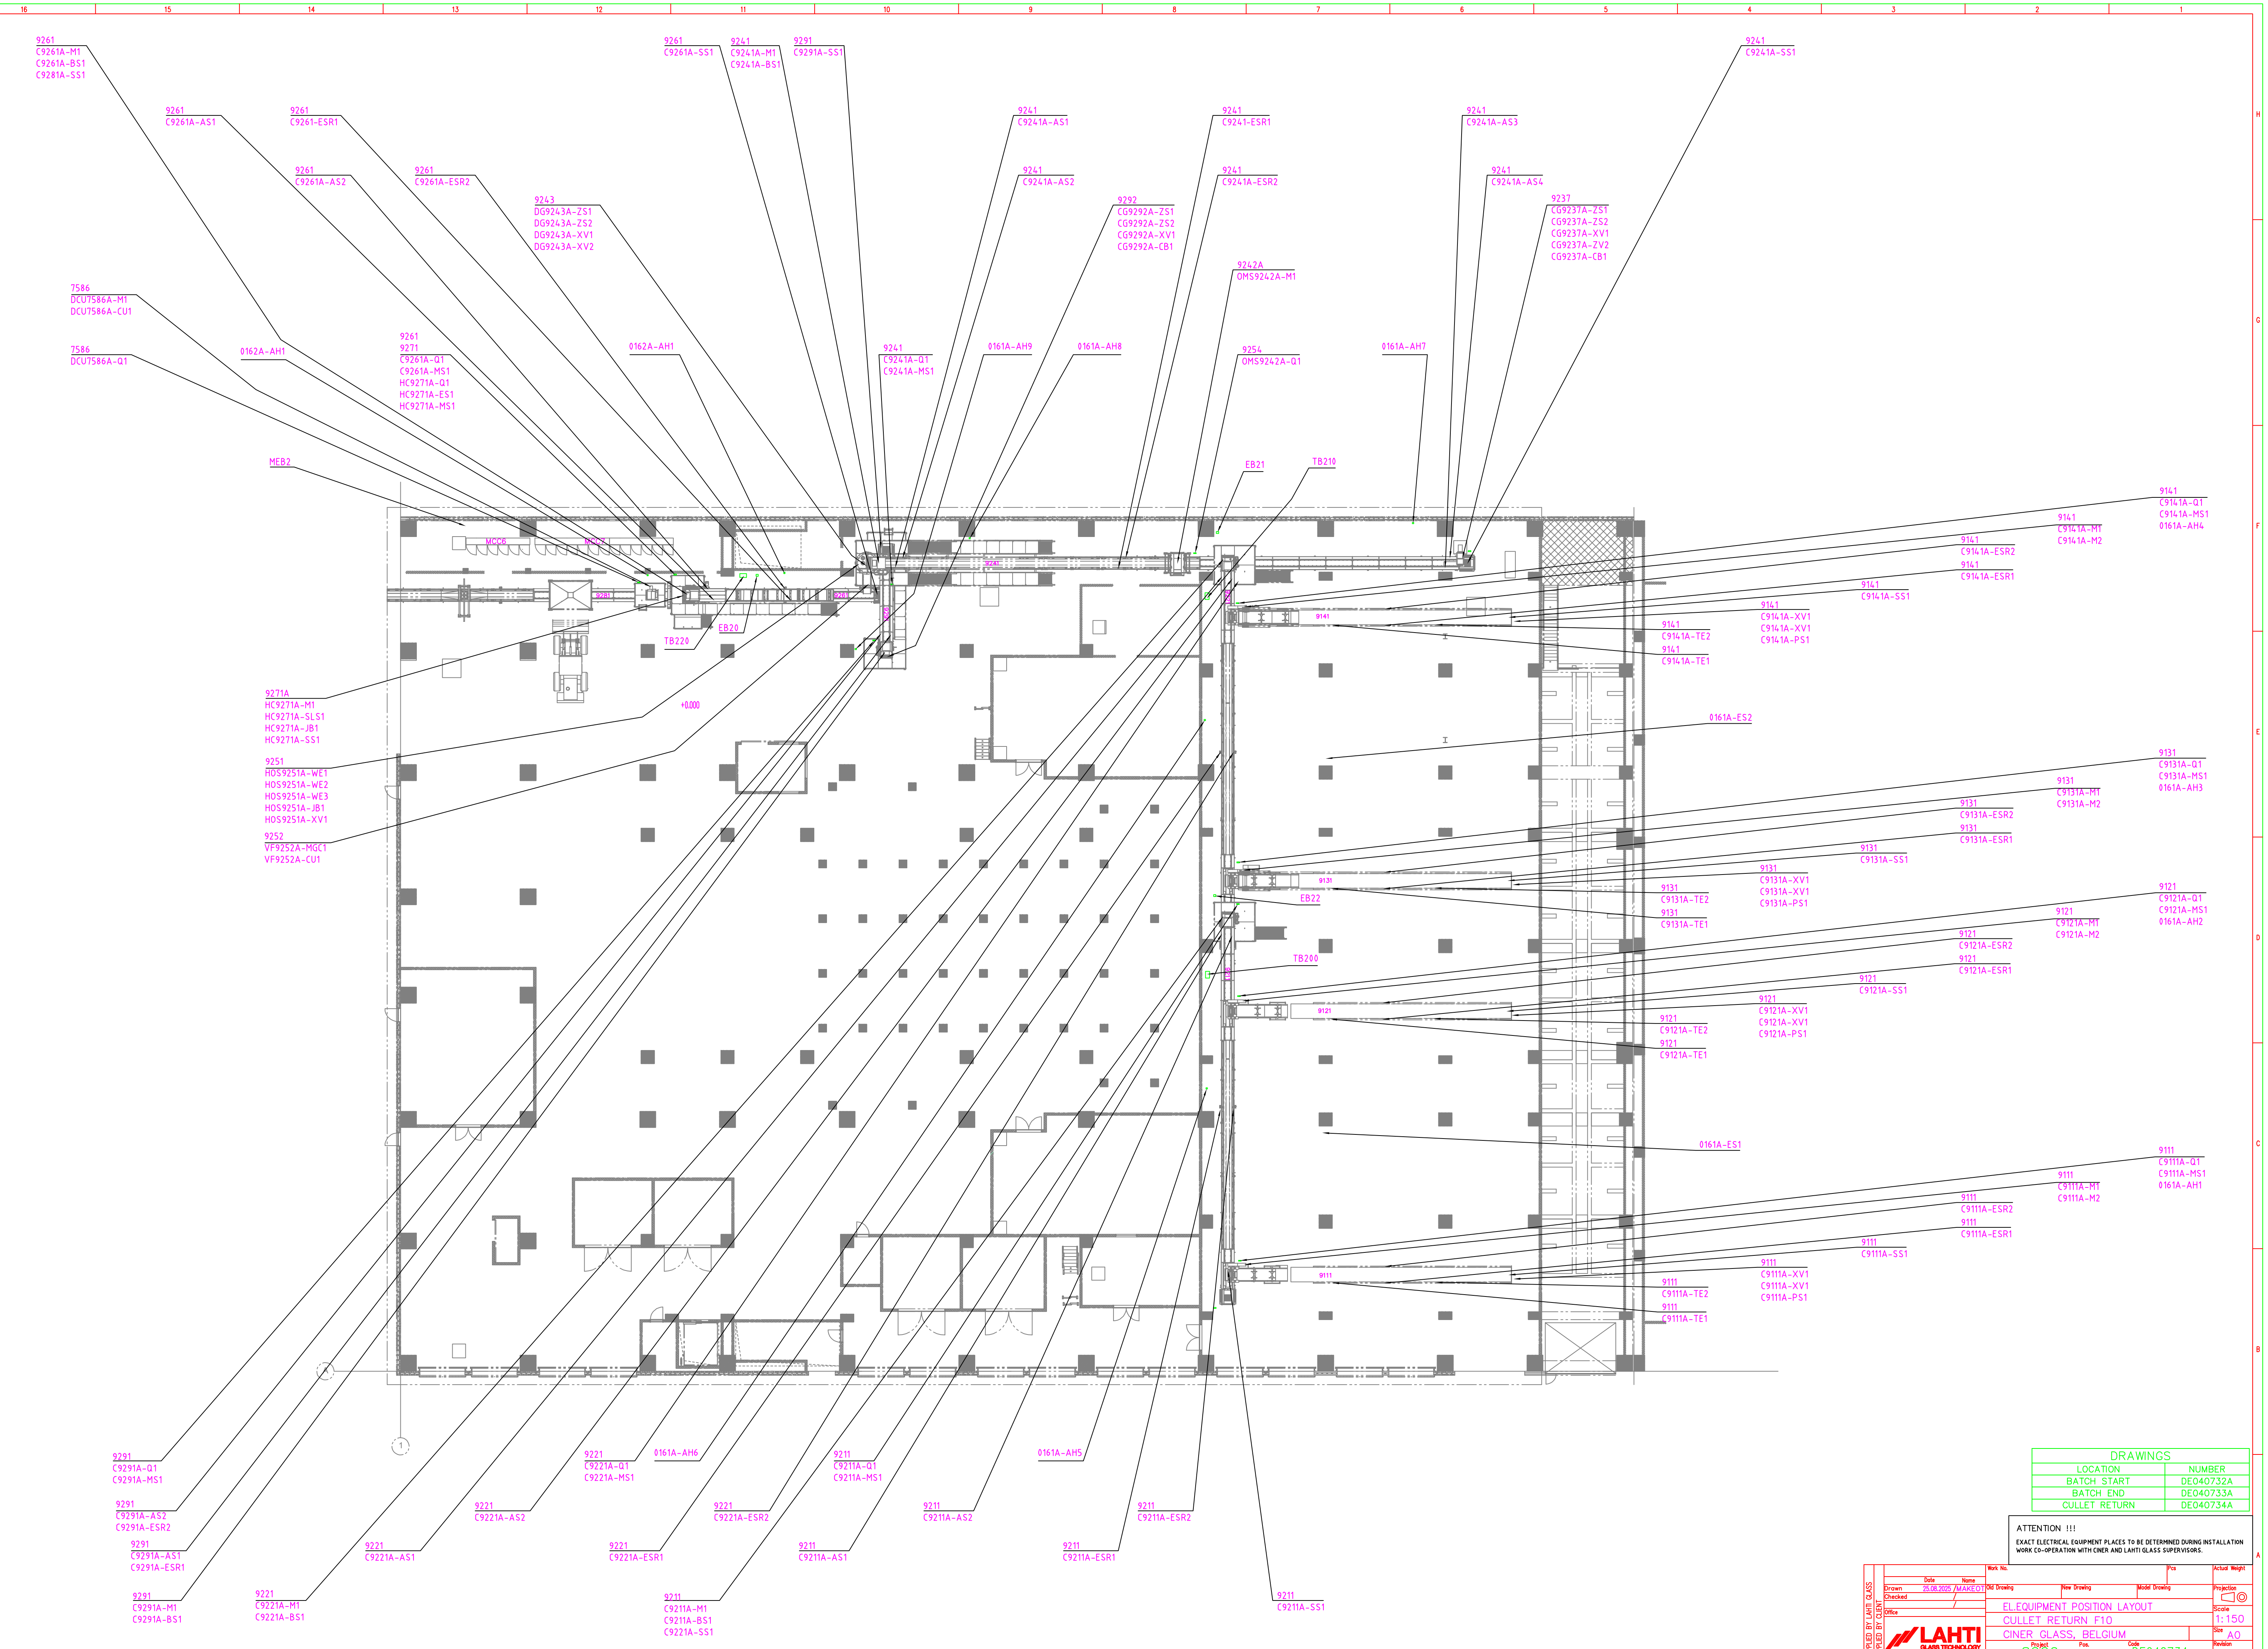

DRAWINGS

LOCATION	NUMBER
BATCH START	DE040732A
BATCH END	DE040733A
CULLET RETURN	DE040734A

ATTENTION !!!

EXACT ELECTRICAL EQUIPMENT PLACES TO BE DETERMINED DURING INSTALLATION WORK CO-OPERATION WITH CINER AND LAHTI GLASS SUPERVISORS.

SUPPLIED BY LAHTI GLASS
SUPPLIED BY CLIENT

	Date	Name
Drawn	25.08.2025	/MAKEOT
Checked		/
		/
Office		

LAHTI GLASS TECHNOLOGY

Work No.
Pcs
Actual Weight
Old Drawing
New Drawing
Model Drawing
Projection

EL.EQUIPMENT POSITION LAYOUT
CULLET RETURN F10
CINER GLASS, BELGIUM

Scale 1:150
Size A0
Revision

Drawing No. Project 8220 Pos. Code DE040734

Printed: 29.09.2025